

ARCHITECT:
LS ARCHITECTURE,
LLC
PH: 702-232-9816
EMAIL: LEISARCH@gmail.com

SEAL:

CONSULTANT:

OWNER:
TIGER REAL
ESTATE LLC

5265 S Durango Dr, Las Vegas, NV 89113
Phone: (702) 742-2373

PROJECT:
WHITE VILLA
@ S. LINDELL RD

REVISIONS:

NO. DATE ISSUE

DRAWING TITLE:


BUILDING 2
FLOOR PLANS &
ELEVATIONS

Project No.: 21150


Date:
Drawn By _____
Author _____
Checked By _____
Checker _____
Approved By _____
Approver _____

File Name: _____

B2-2

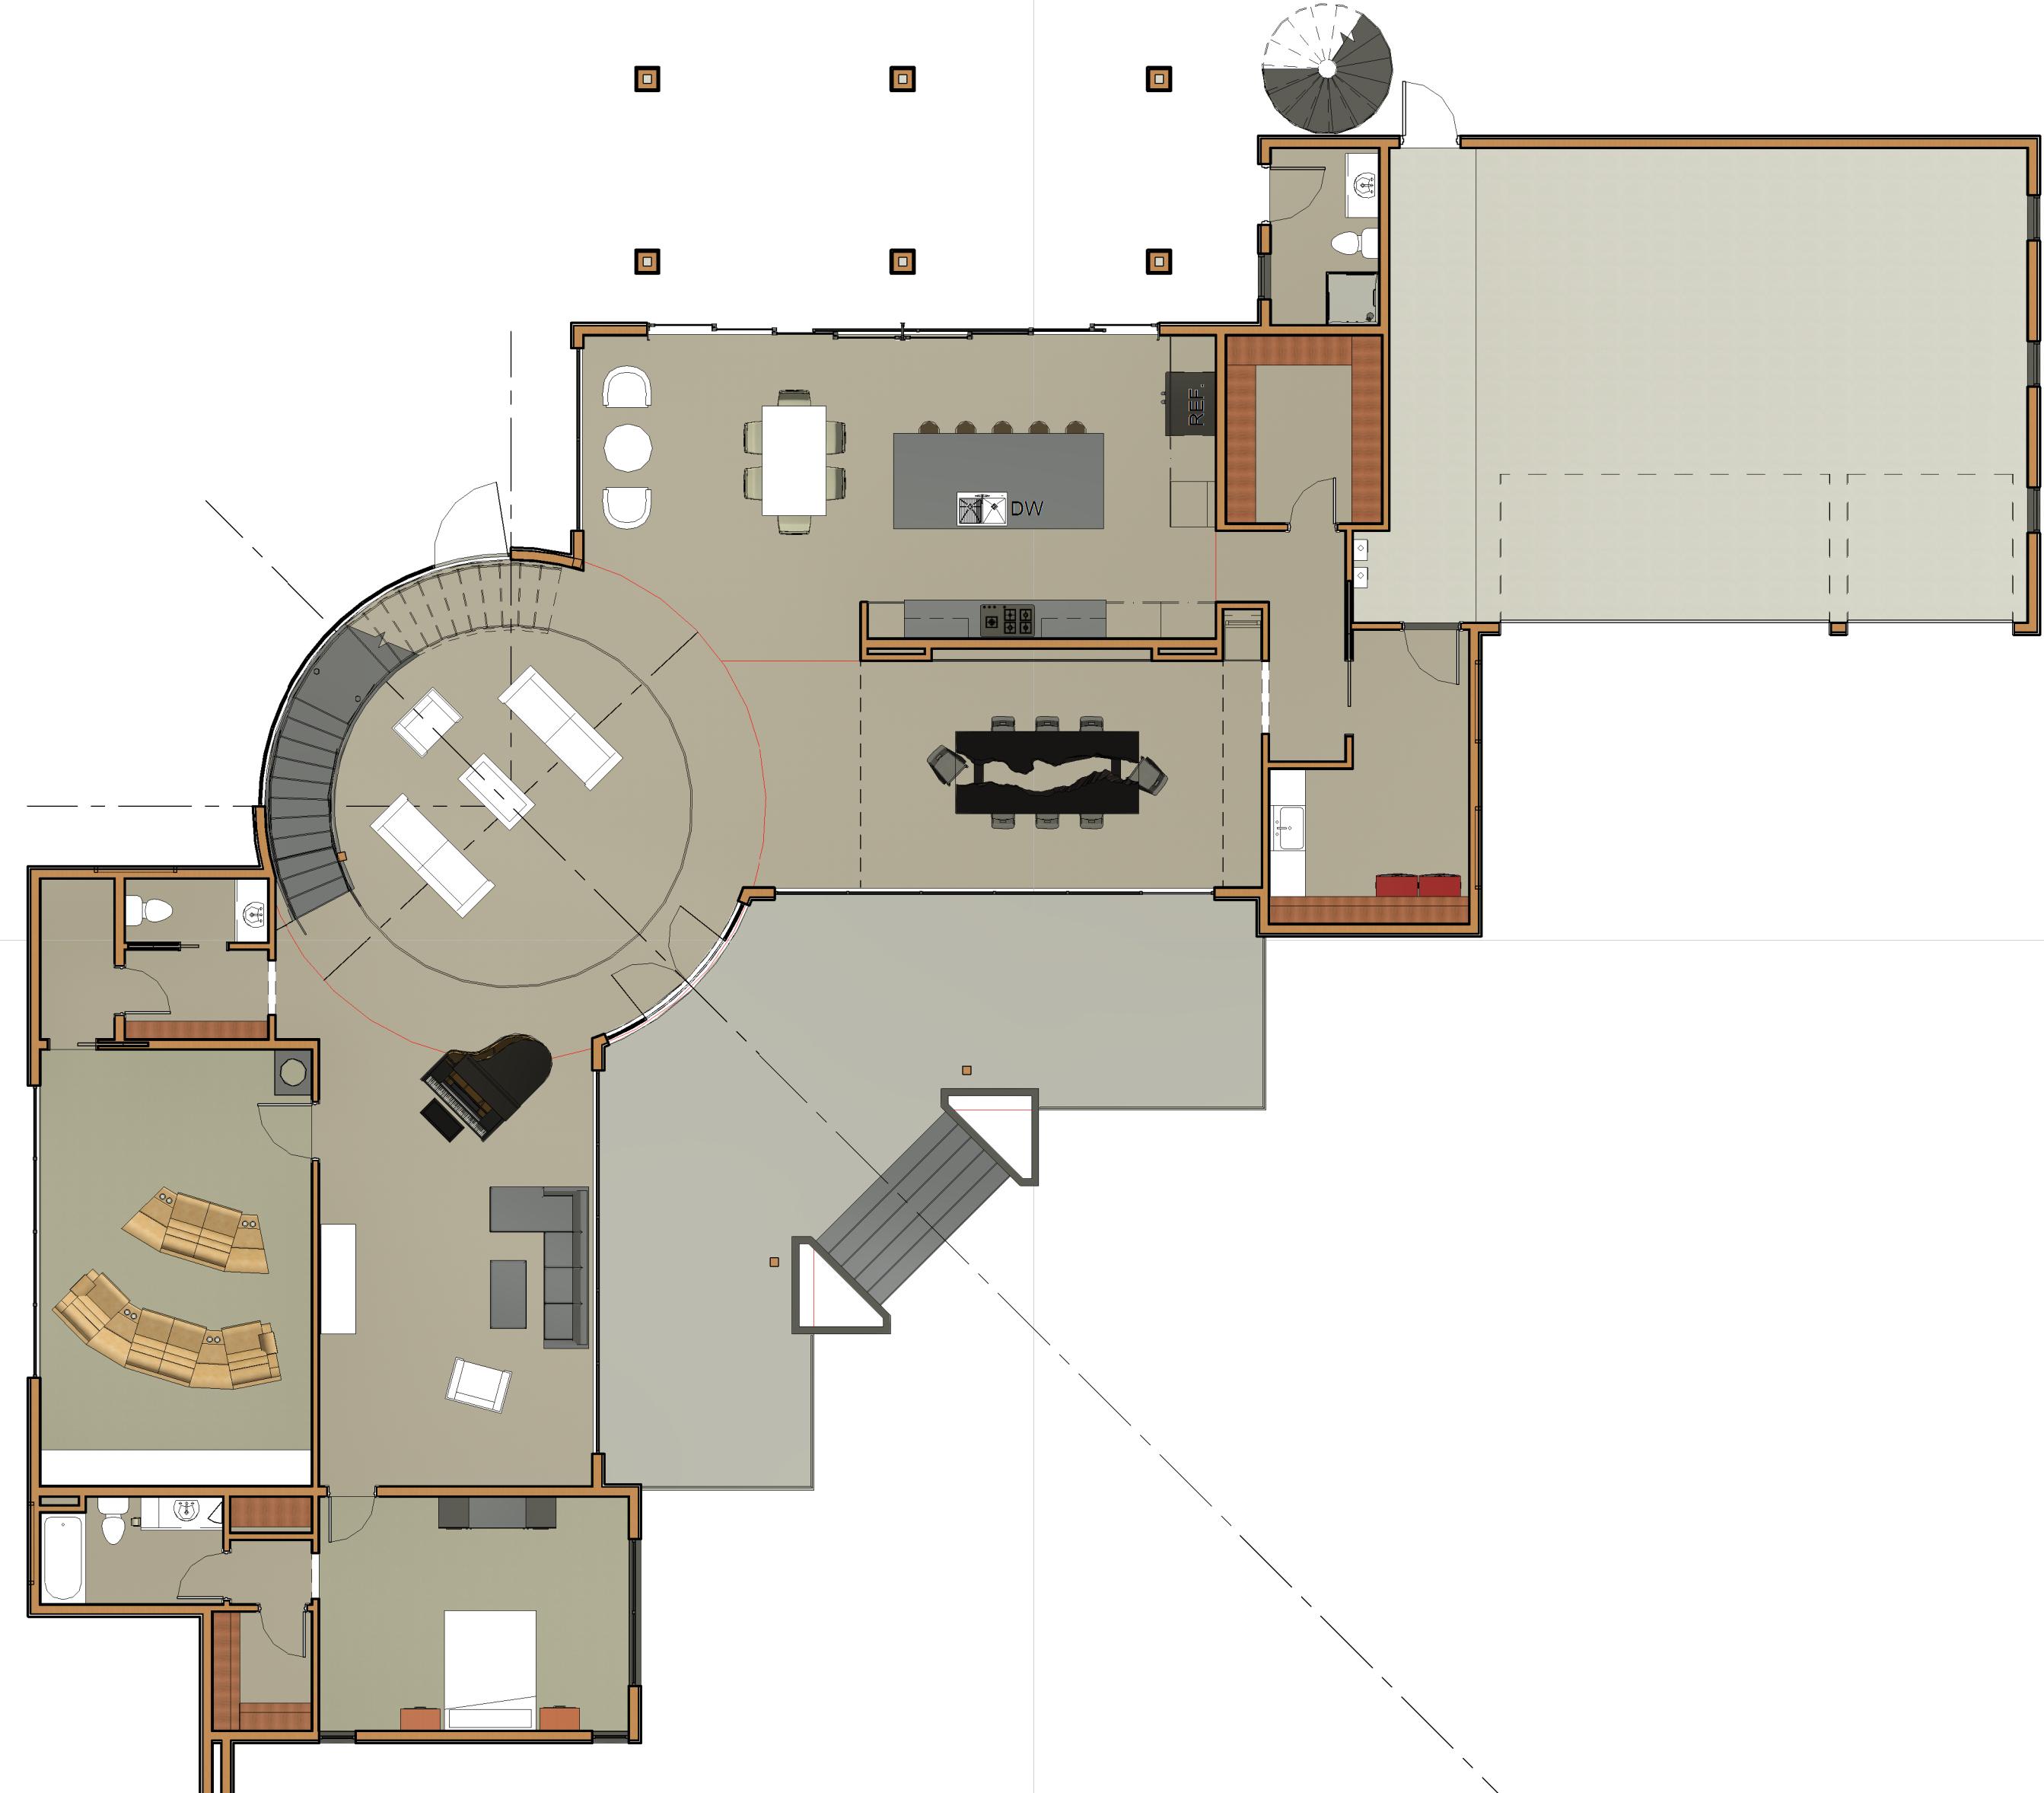

1 DESIGN - BUILDING 2 - FIRST LEVEL FLOOR PLAN
1/8" = 1'-0"

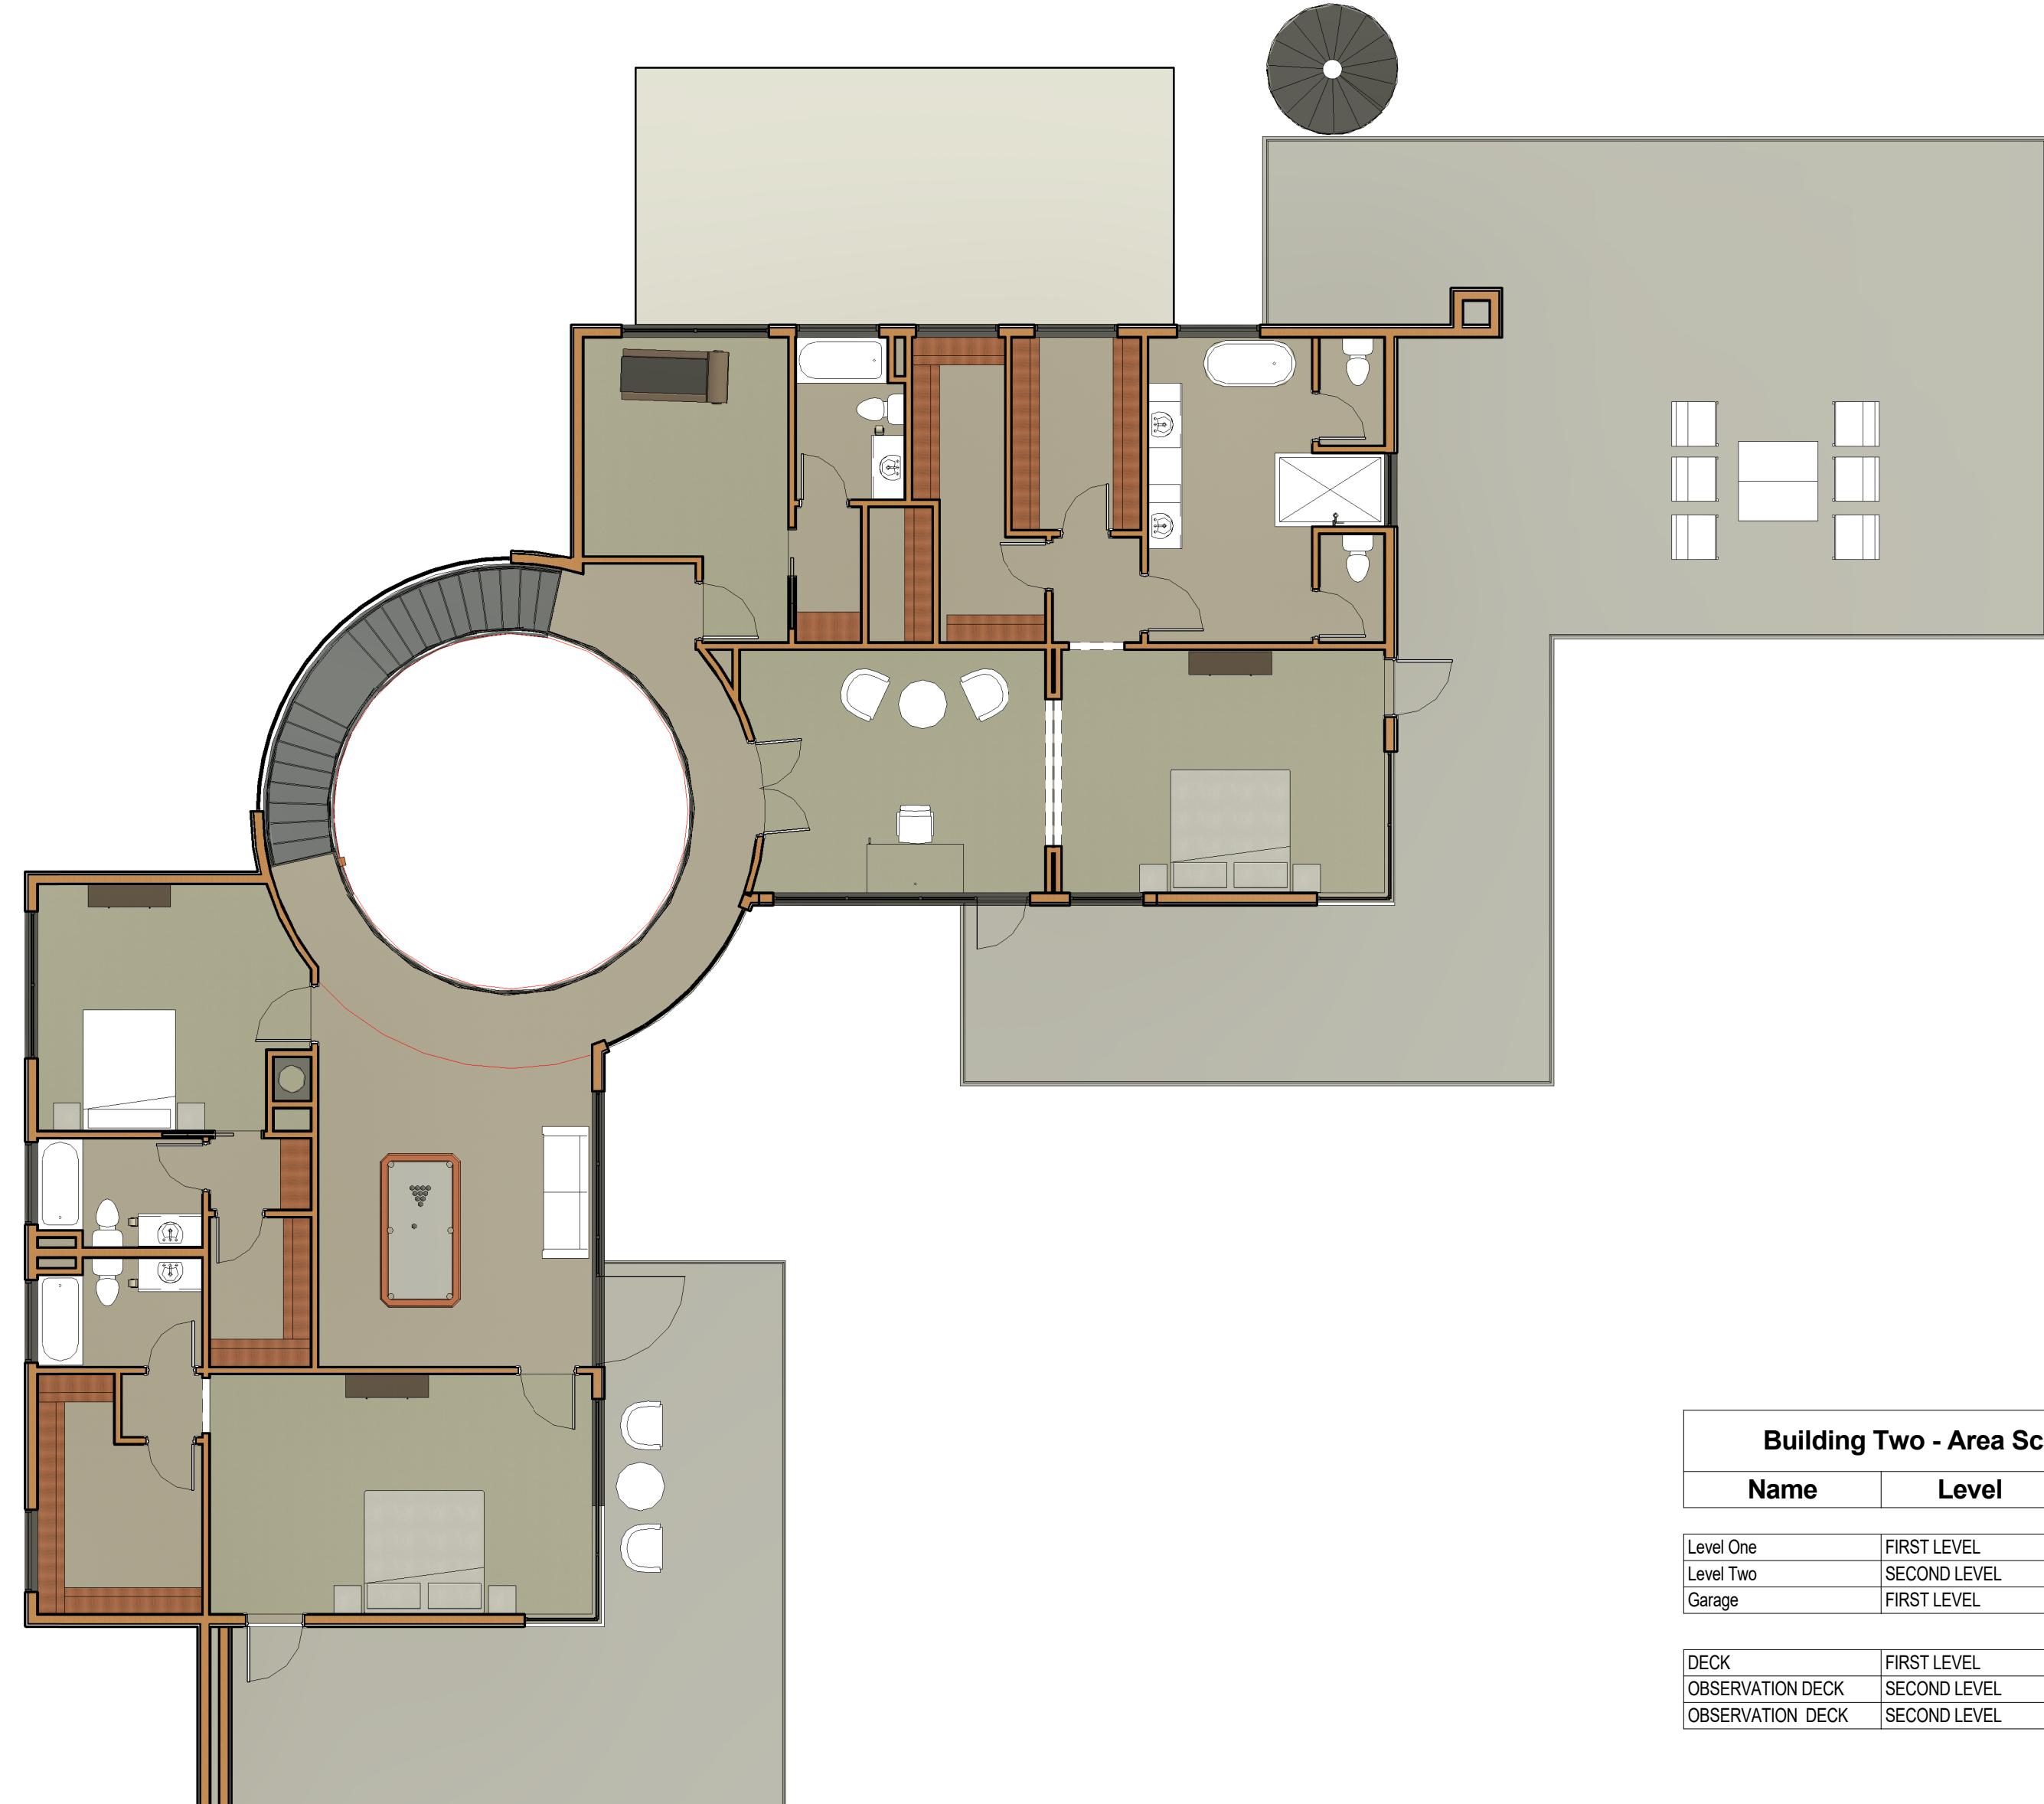

2 DESIGN - BUILDING 2 - SECOND LEVEL FLOOR PLAN
1/8" = 1'-0"



3 EXTERIOR ELEVATION
1/8" = 1'-0"



4 EXTERIOR ELEVATION
1/8" = 1'-0"



5 EXTERIOR ELEVATION
1/8" = 1'-0"



6 EXTERIOR ELEVATION
1/8" = 1'-0"