

ARCHITECT:  
**LS ARCHITECTURE**  
 LLC  
 PH: 702-232-9816  
 EMAIL: LEISARCH@GMAIL.COM  
 SEAL:  
 CONSULTANT:  
 OWNER:  
 TIGER REAL  
 ESTATE LTD  
 5265 S Durango Dr. Las Vegas, NV 89113  
 Phone: (702) 742-2373


# WHITE VILLA

@ S. LINDELL RD


DRAWING TITLE:  
**BUILDING 1**  
 FLOOR PLANS &  
 ELEVATIONS  
 Drawing notes to consider before project copy or print:  
 - Drawing must be copied at true scale.  
 - Drawing must be oriented to North.  
 - Do not change dimensions, levels, spans, and floor conditions and do not alter it in any way.  
 Project No.: 21150  
 Date:  
 Drawn By \_\_\_\_\_ Checked By \_\_\_\_\_ DATE  
 Author \_\_\_\_\_ Checker \_\_\_\_\_ Approver \_\_\_\_\_  
 File Name:



2 BUILDING 2 - SECOND LEVEL FLOOR PLAN

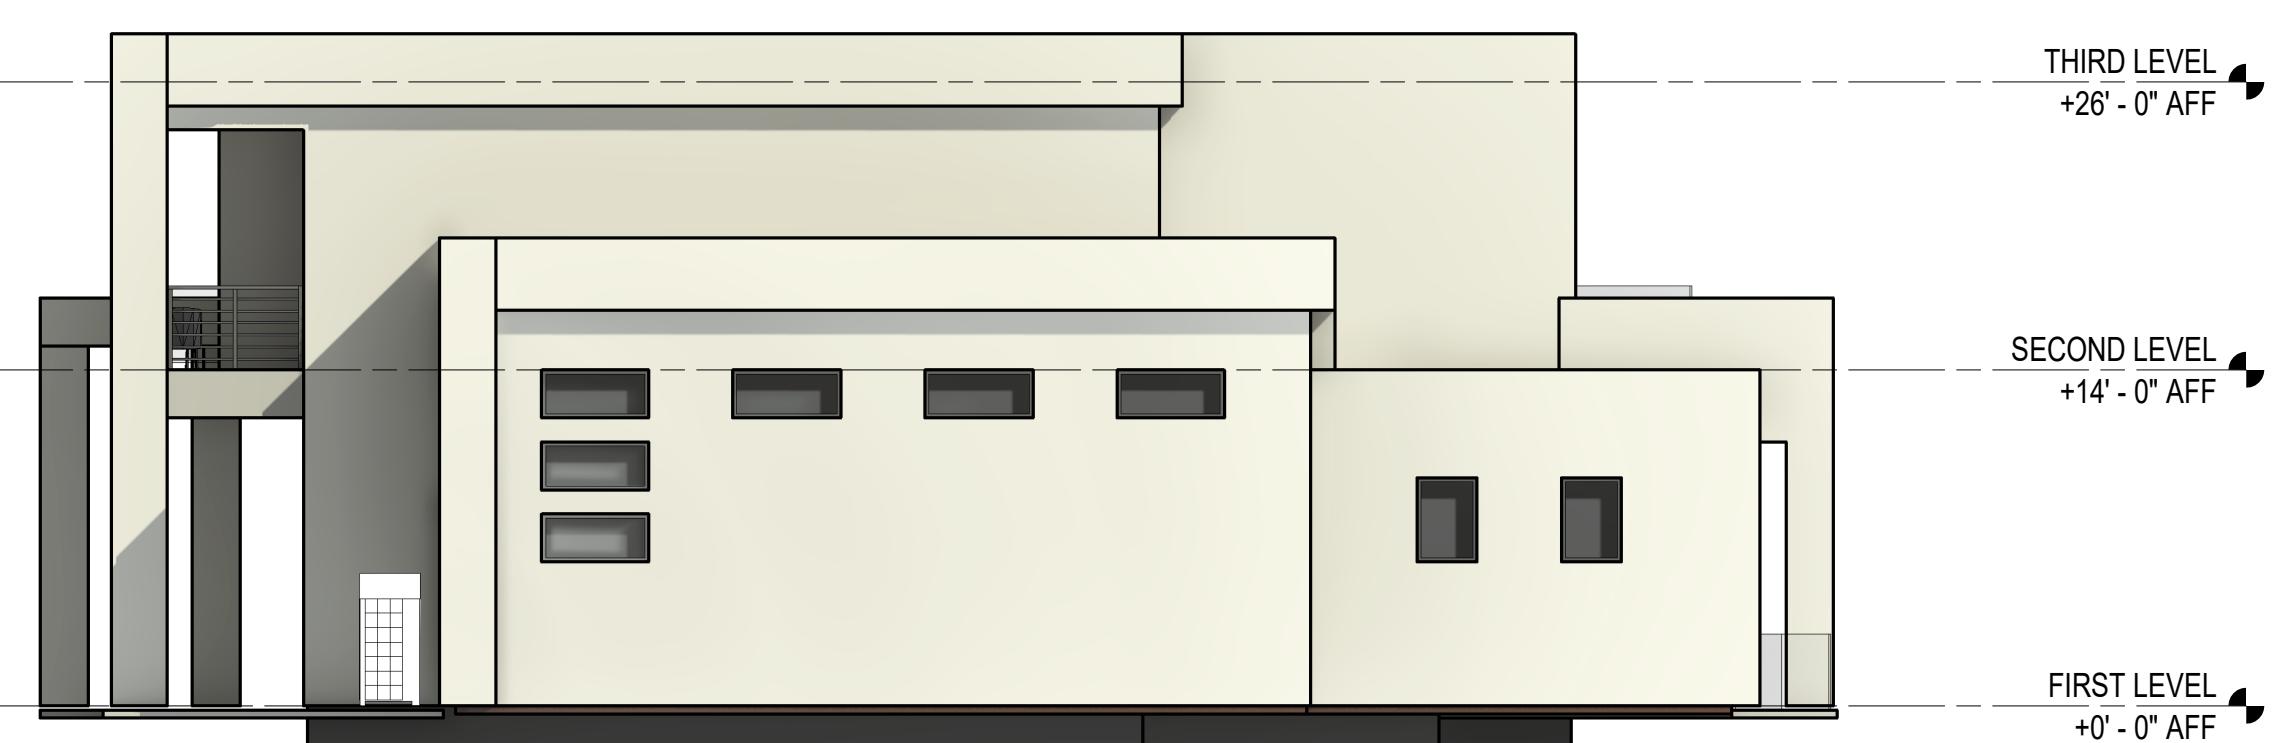

4 Elevation 2 - a

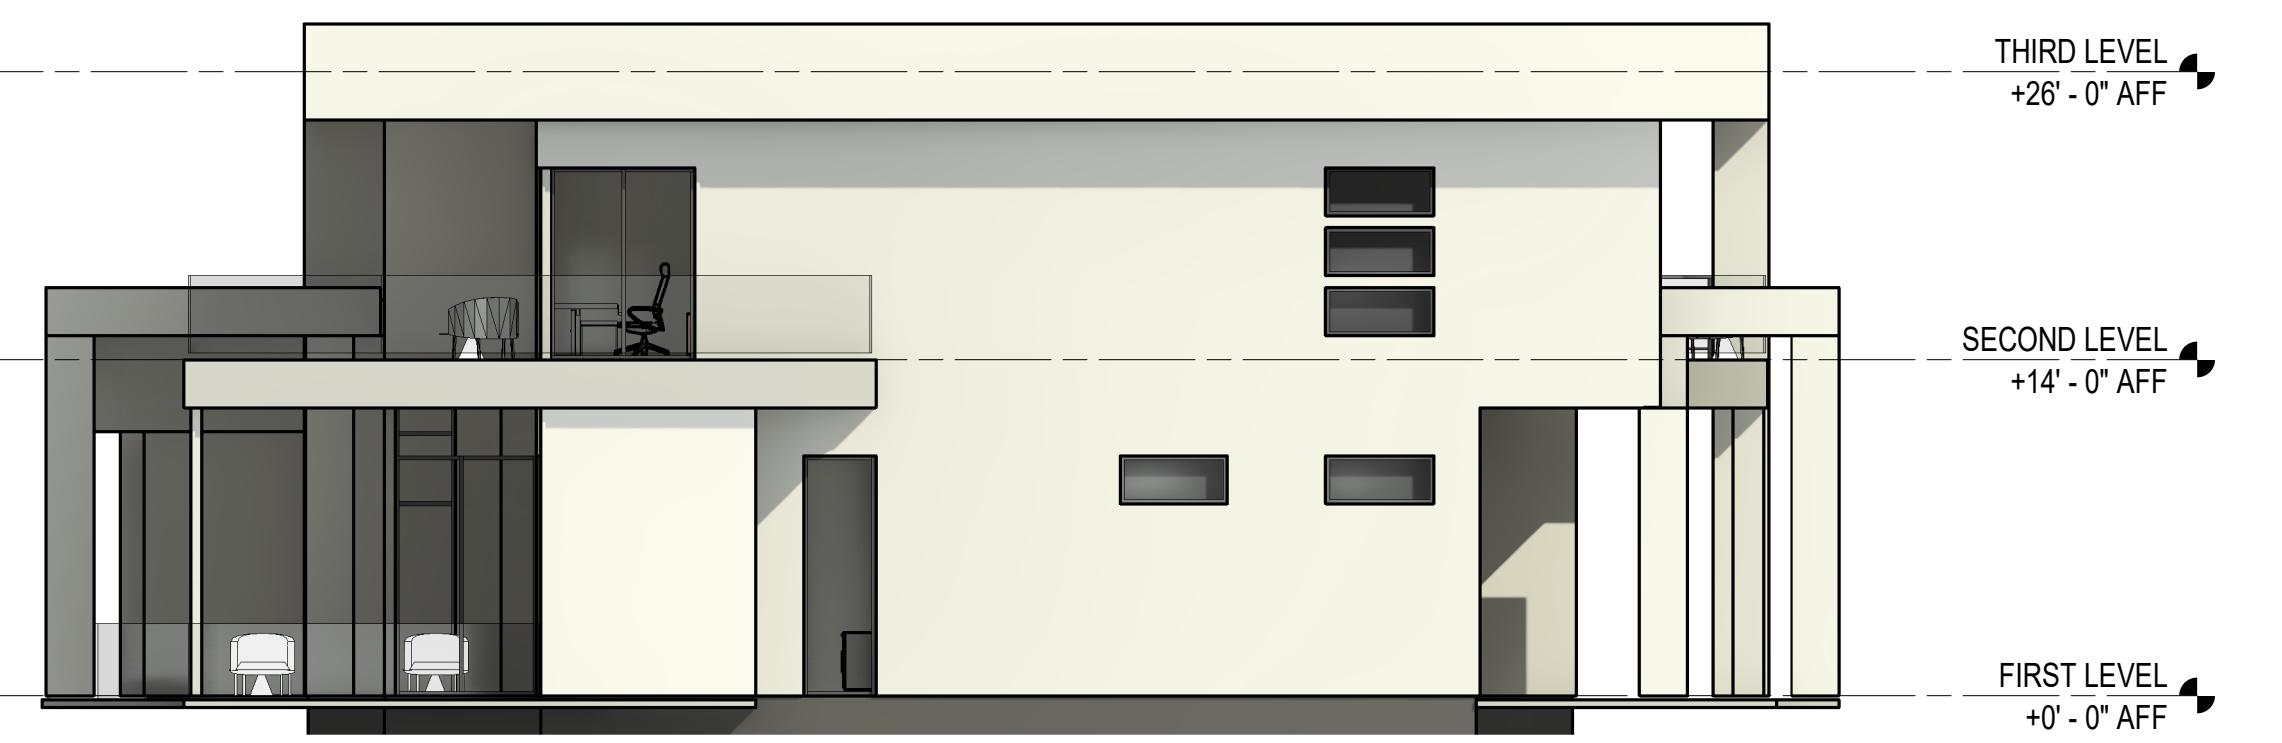

6 Elevation 4 - a



Building One - Area Schedule		
Name	Level	Area
LEVEL ONE	FIRST LEVEL	3,421 SF
LEVEL TWO	SECOND LEVEL	2,676 SF
3-CAR GARAGE	FIRST LEVEL	1,128 SF
DECK	FIRST LEVEL	1,094 SF
OBSERVATION DECK	SECOND LEVEL	446 SF
OBSERVATION DECK	SECOND LEVEL	563 SF
		2,103 SF

1 DESIGN - BUILDING 1 - FIRST LEVEL PLAN



3 Elevation 1 - a



5 Elevation 3 - a